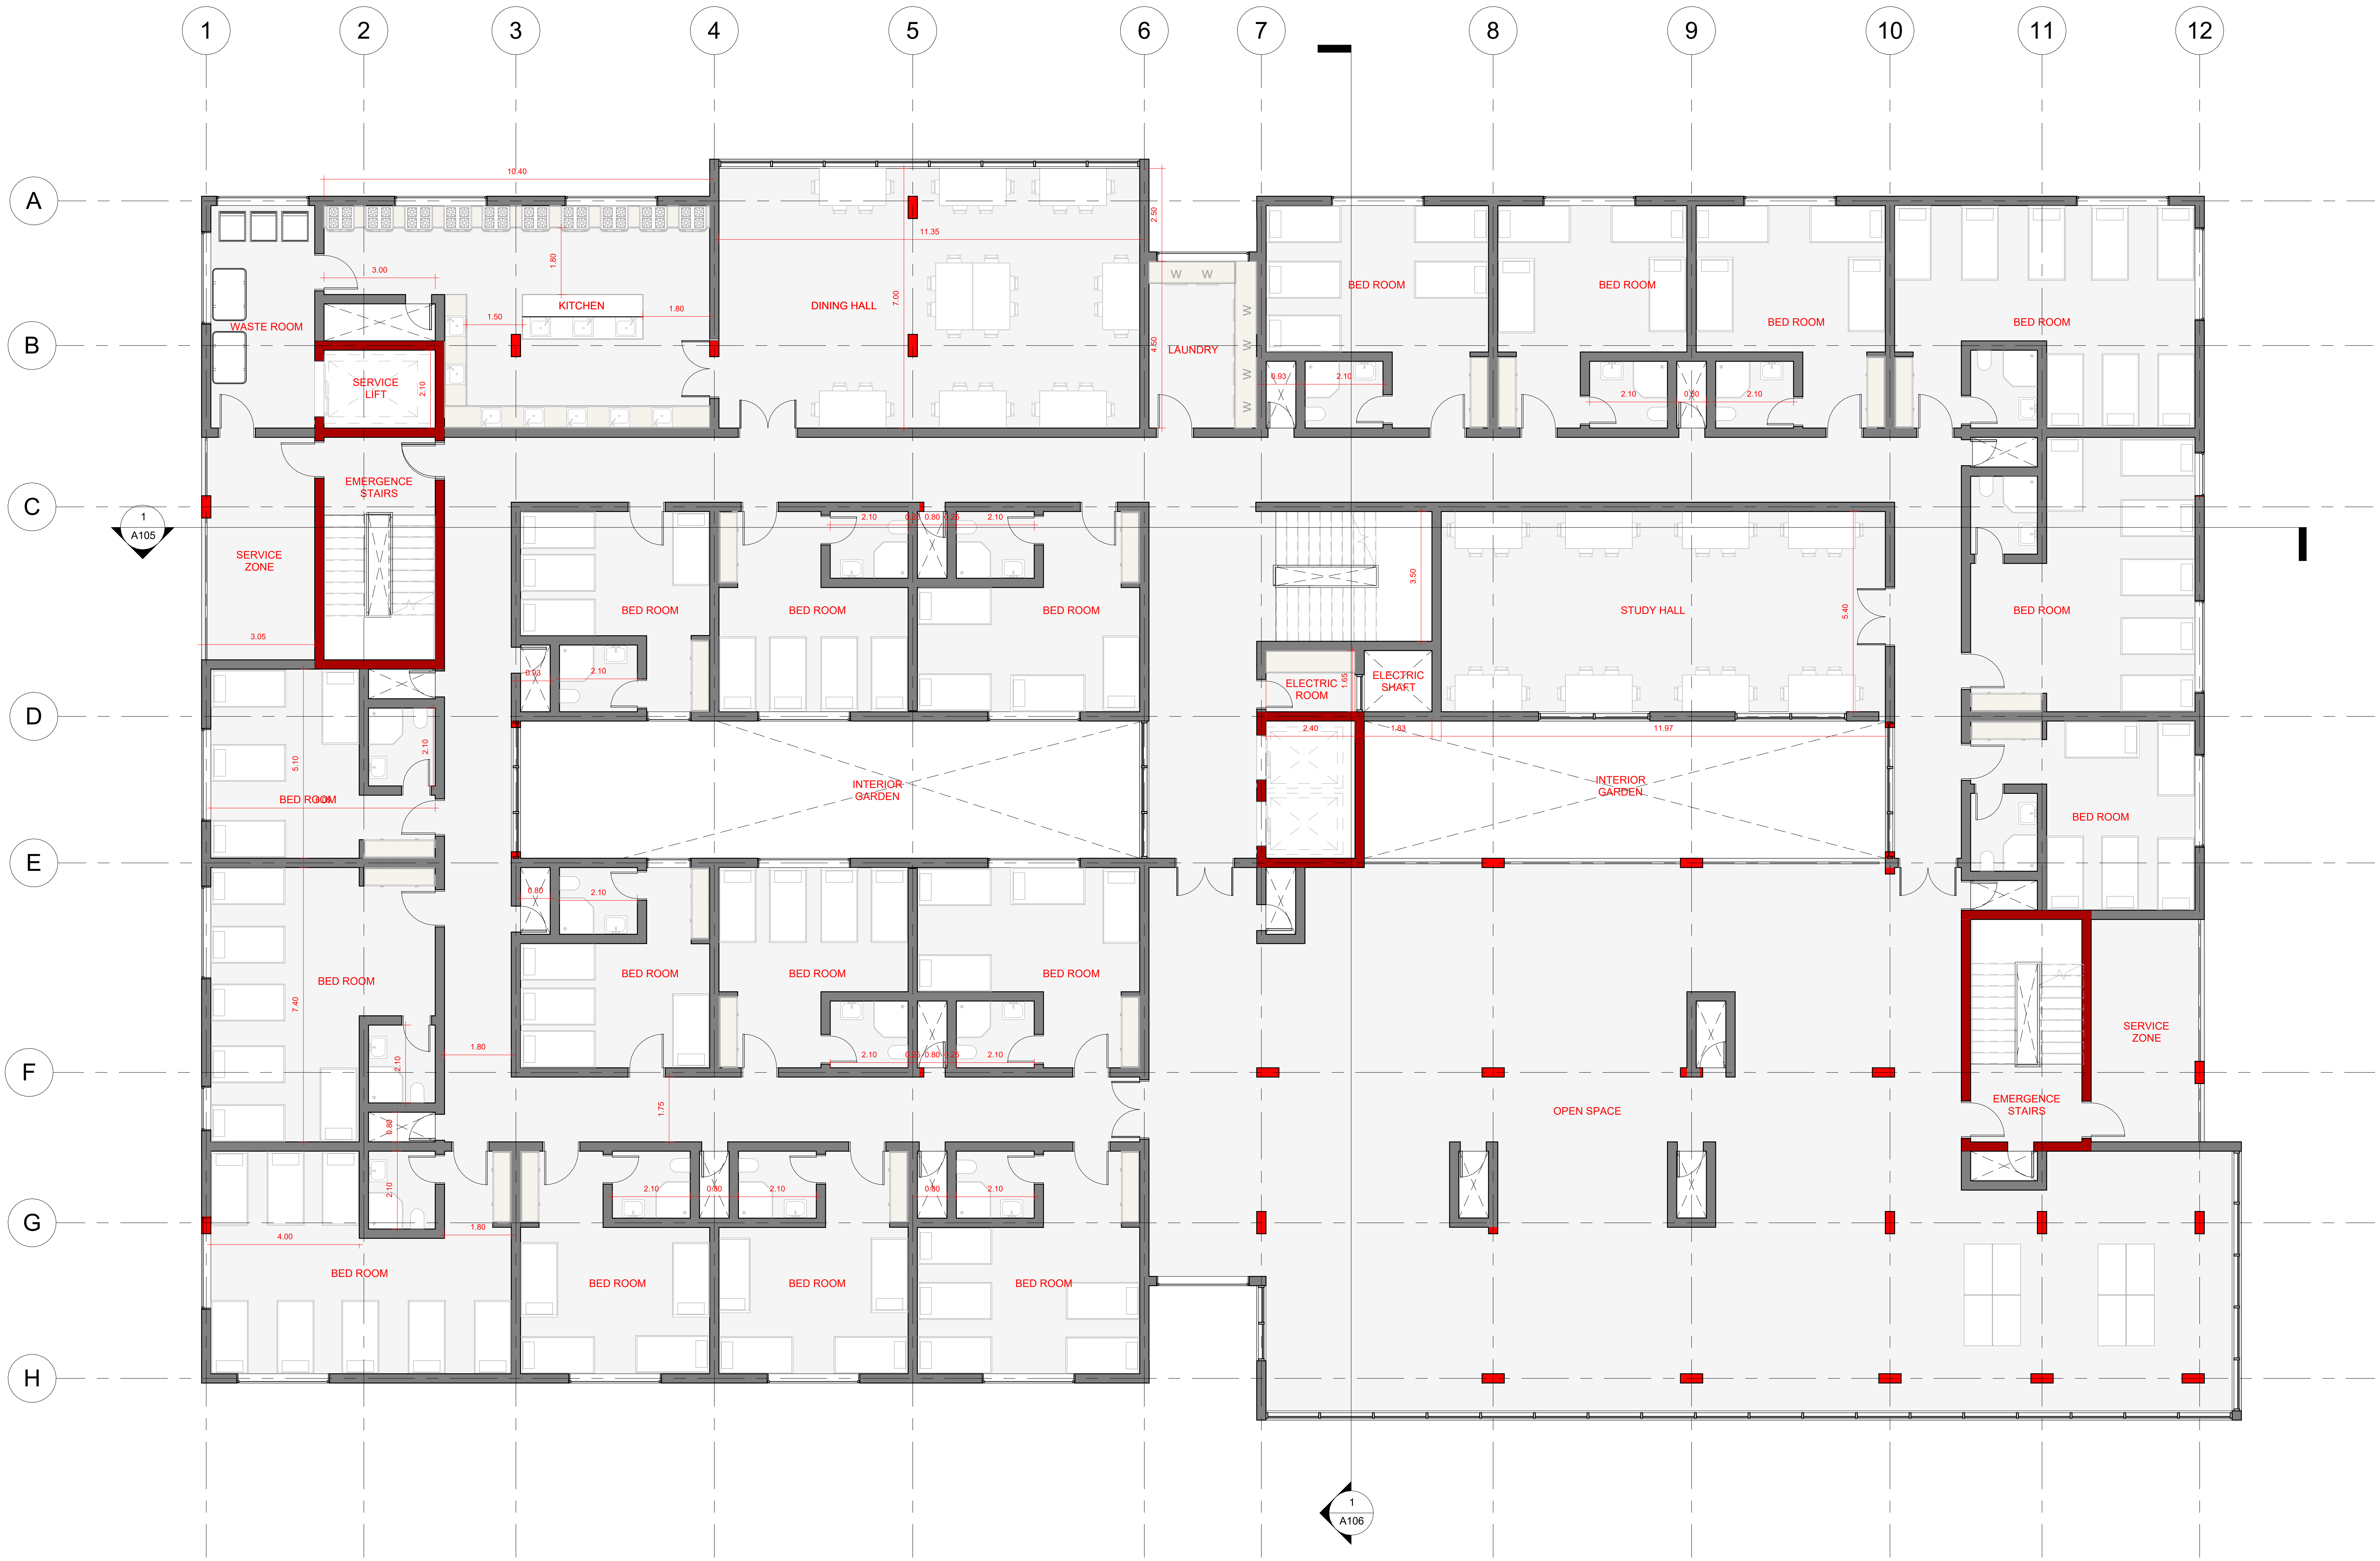
1
2
3
4
5
6
7
8
9
10
11
12
A
B
C
D
E
F
G
H
10.40
11.35
WASTE ROOM
KITCHEN
3.00
1.80
1.50
1.80
SERVICE LIFT
2.10
DINING HALL
7.00
2.50
4.50
LAUNDRY
BED ROOM
BED ROOM
BED ROOM
BED ROOM
0.93
2.10
2.10
0.80
2.10
EMERGENCE STAIRS
SERVICE ZONE
3.05
1
A105
BED ROOM
BED ROOM
BED ROOM
BED ROOM
0.93
2.10
STUDY HALL
3.50
5.40
ELECTRIC ROOM
ELECTRIC SHAFT
1.65
2.40
1.83
11.97
BED ROOM
5.10
2.10
INTERIOR GARDEN
INTERIOR GARDEN
BED ROOM
BED ROOM
BED ROOM
BED ROOM
BED ROOM
BED ROOM
7.40
0.80
2.10
1.80
1.75
2.10
0.80
2.10
SERVICE ZONE
EMERGENCE STAIRS
OPEN SPACE
BED ROOM
BED ROOM
BED ROOM
BED ROOM
4.00
1.80
2.10
0.80
2.10
1
A106